

Plano de vivienda · Instalación eléctrica interior

Planta general · Electrificación básica (5.750 W · 230 V) · REBT ITC-BT-25

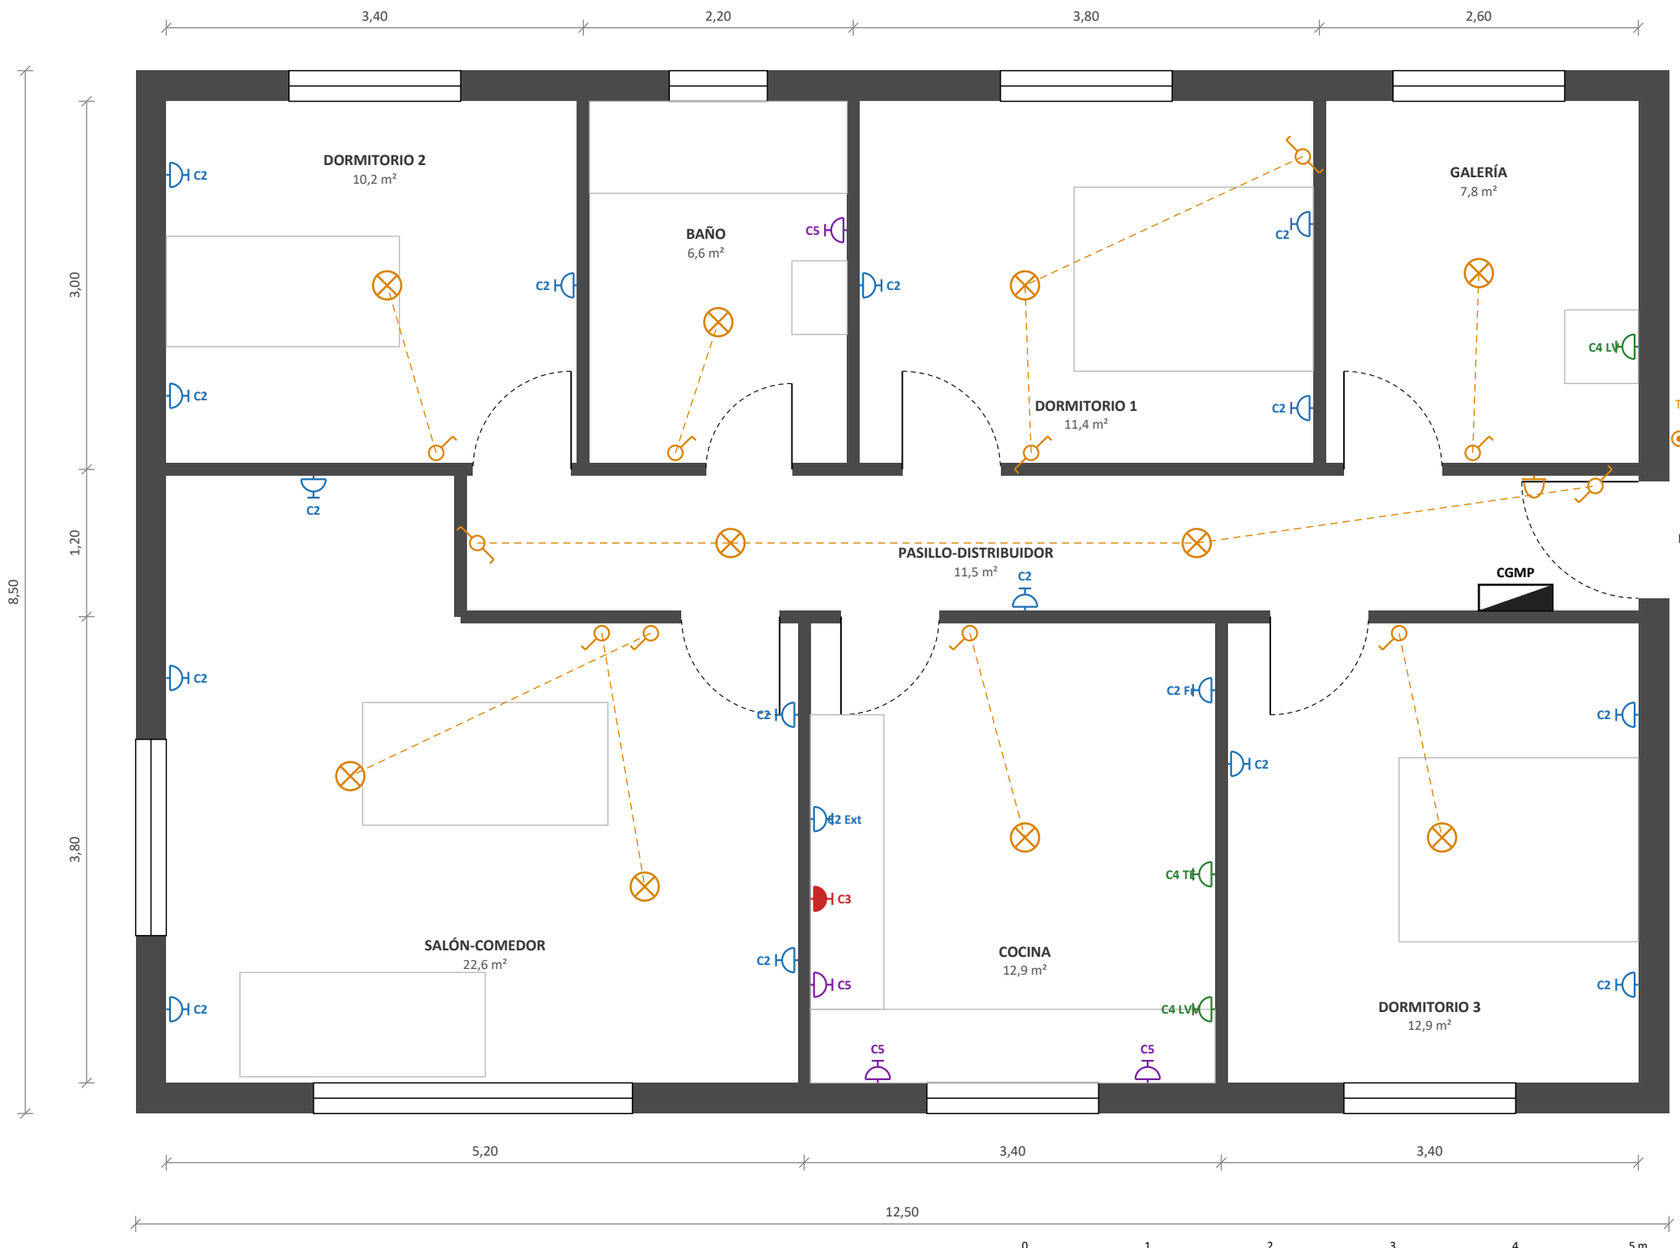

Esquema unifilar del CGMP

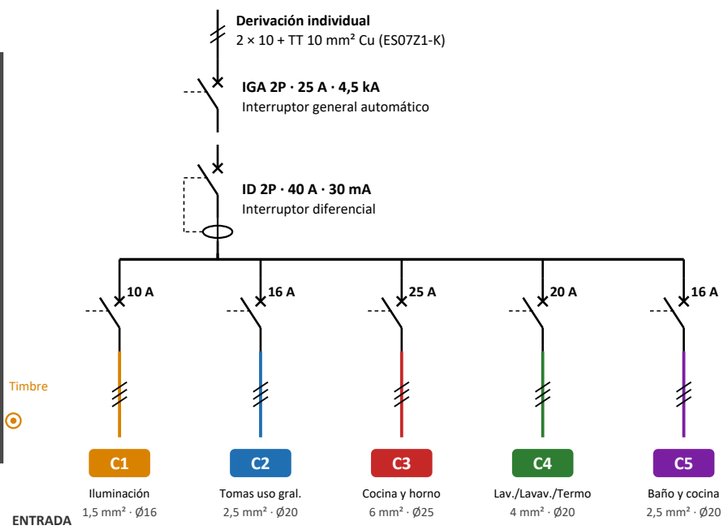

Circuitos interiores (ITC-BT-25, tabla 1)

Circ.	Destino	PIA	Sección	Tubo	Puntos
C1	Iluminación	10 A	1,5 mm²	Ø16	10 luz
C2	Tomas de uso general	16 A	2,5 mm²	Ø20	17 tomas
C3	Cocina y horno	25 A	6 mm²	Ø25	1 toma
C4	Lavadora, lavavajillas, termo	20 A	4 mm²	Ø20	3 tomas
C5	Baño y cocina (encimera)	16 A	2,5 mm²	Ø20	4 tomas

- Conductores H07V-K 450/750 V; fase marrón/negro/gris, neutro azul, protección verde-amarillo.
- Tubos empotrados flexibles corrugados; mecanismos a 1,10 m, tomas a 0,30 m (encimera de cocina a 1,10 m).
- Baño: respetar volúmenes de protección (ITC-BT-27).
- Conductor de protección en todos los circuitos.

Leyenda

- Punto de luz en techo
- Interruptor unipolar 10 A
- Conmutador 10 A
- Pulsador (timbre)
- Timbre
- Mando de punto de luz
- Base 16 A 2P+T
- Base 25 A 2P+T (cocina-horno)
- Cuadro general de mando y protección
- C4 LV — LV lavadora · LVV lavavajillas
- C4 TE — TE termo · Fr frigorífico · Ext extractor
- Mobiliario orientativo en gris

Color del símbolo = circuito: C1 Iluminación · C2 Tomas uso general · C3 Cocina y horno · C4 Lavadora, lavavajillas, termo · C5 Baño y cocina

Escala 1:50 0 1 2 3 4 5 m

Plano: Vivienda · Instalación eléctrica	
Nombre:	
Curso:	Fecha:
Plano 01 · Planta	Formato A3 · Escala 1:50